

CURVE DATA TABLE						CURVE DATA TABLE						CURVE DATA TABLE					
CURVE	LENGTH	RADIUS	CURVE	LENGTH	RADIUS	CURVE	LENGTH	RADIUS	CURVE	LENGTH	RADIUS	CURVE	LENGTH	RADIUS	CURVE	LENGTH	RADIUS
C1	18.85'	12.00'	C25	133.68'	465.00'	C49	21.03'	25.00'	C1	18.85'	12.00'	C25	133.68'	465.00'	C49	21.03'	25.00'
C2	14.35'	50.00'	C26	143.51'	465.00'	C50	12.83'	12.00'	C2	14.35'	50.00'	C26	143.51'	465.00'	C50	12.83'	12.00'
C3	21.79'	50.00'	C27	35.11'	465.00'	C51	55.08'	65.00'	C3	21.79'	50.00'	C27	35.11'	465.00'	C51	55.08'	65.00'
C4	80.85'	50.00'	C28	18.16'	465.00'	C52	12.41'	12.00'	C4	80.85'	50.00'	C28	18.16'	465.00'	C52	12.41'	12.00'
C5	52.17'	50.00'	C29	78.19'	465.00'	C53	235.68'	255.00'	C5	52.17'	50.00'	C29	78.19'	465.00'	C53	235.68'	255.00'
C6	86.70'	50.00'	C30	110.85'	535.00'	C54	17.33'	12.00'	C6	86.70'	50.00'	C30	110.85'	535.00'	C54	17.33'	12.00'
C7	9.63'	50.00'	C31	62.81'	325.00'	C55	20.37'	12.00'	C7	9.63'	50.00'	C31	62.81'	325.00'	C55	20.37'	12.00'
C8	36.14'	50.00'	C32	198.16'	325.00'				C8	36.14'	50.00'	C32	198.16'	325.00'			
C9	18.85'	12.00'	C33	55.60'	25.00'				C9	18.85'	12.00'	C33	55.60'	25.00'			
C10	106.46'	600.00'	C34	72.64'	50.00'				C10	106.46'	600.00'	C34	72.64'	50.00'			
C11	191.16'	600.00'	C35	61.18'	50.00'				C11	191.16'	600.00'	C35	61.18'	50.00'			
C12	65.06'	700.00'	C36	48.37'	50.00'				C12	65.06'	700.00'	C36	48.37'	50.00'			
C13	108.82'	700.00'	C37	33.23'	50.00'				C13	108.82'	700.00'	C37	33.23'	50.00'			
C14	100.09'	700.00'	C38	45.08'	25.00'				C14	100.09'	700.00'	C38	45.08'	25.00'			
C15	73.26'	700.00'	C39	63.97'	65.00'				C15	73.26'	700.00'	C39	63.97'	65.00'			
C16	17.80'	12.00'	C40	10.97'	12.00'				C16	17.80'	12.00'	C40	10.97'	12.00'			
C17	17.80'	12.00'	C41	118.65'	215.00'				C17	17.80'	12.00'	C41	118.65'	215.00'			
C18	108.85'	340.00'	C42	157.27'	285.00'				C18	108.85'	340.00'	C42	157.27'	285.00'			
C19	26.91'	340.00'	C43	25.38'	12.00'				C19	26.91'	340.00'	C43	25.38'	12.00'			
C20	42.66'	535.00'	C44	21.03'	25.00'				C20	42.66'	535.00'	C44	21.03'	25.00'			
C21	186.56'	535.00'	C45	81.83'	50.00'				C21	186.56'	535.00'	C45	81.83'	50.00'			
C22	35.65'	535.00'	C46	63.46'	50.00'				C22	35.65'	535.00'	C46	63.46'	50.00'			
C23	44.71'	535.00'	C47	49.83'	50.00'				C23	44.71'	535.00'	C47	49.83'	50.00'			
C24	49.72'	535.00'	C48	46.08'	50.00'				C24	49.72'	535.00'	C48	46.08'	50.00'			

LEGEND

--- BLOCK BOUNDARY

--- PROPOSED MULTI-USE PATH

R.O.W. RIGHT OF WAY

N.A.O.S. NATURAL AREA

OPEN SPACE (PRIVATE)

O/S COMMON OPEN SPACE (PUBLIC)

N.V.A.E. NON VEHICULAR ACCESS EASEMENT


↔ DUAL ACCESS DRIVEWAY

BLOCK 14 LOT DATA TABLE		
No.	LOT AREA	
1	10,648 Sq Ft	0.24 Ac.
2	10,709 Sq Ft	0.25 Ac.
3	10,049 Sq Ft	0.23 Ac.
4	11,245 Sq Ft	0.26 Ac.
5	11,245 Sq Ft	0.26 Ac.
6	10,049 Sq Ft	0.23 Ac.
7	10,049 Sq Ft	0.23 Ac.
8	11,245 Sq Ft	0.26 Ac.
9	11,245 Sq Ft	0.26 Ac.
10	10,049 Sq Ft	0.23 Ac.
11	10,049 Sq Ft	0.23 Ac.
12	11,245 Sq Ft	0.26 Ac.
13	11,245 Sq Ft	0.26 Ac.
14	10,049 Sq Ft	0.23 Ac.
15	10,049 Sq Ft	0.23 Ac.
16	11,245 Sq Ft	0.26 Ac.
17	16,422 Sq Ft	0.38 Ac.
18	11,816 Sq Ft	0.27 Ac.
19	13,613 Sq Ft	0.31 Ac.
20	19,228 Sq Ft	0.44 Ac.
21	23,053 Sq Ft	0.53 Ac.

SITE DATA TABLE					
BLOCK No.	ZONING	GROSS AREA (ACRES)	NUMBER OF LOTS	GROSS DENSITY LOTS/ACRE	AREA IN R.O.W. (ACRES)
12	M-2	1.542	2	1.29	0
13	M-2	6.676	11	1.65	0.334
14	R1-8	6.510	21	3.23	0.667
15	R1-18(1)	18.443	18	0.98	0.424
16	R1-18	14.570	11	0.75	0.281
17	M-2	13.163	7	0.53	4.713

NOTES:

(1) LOTS ADJACENT TO THE SOUTHERLY LINE OF BLOCK 15 SHALL HAVE A MINIMUM AREA OF 44,000 SQUARE FEET.

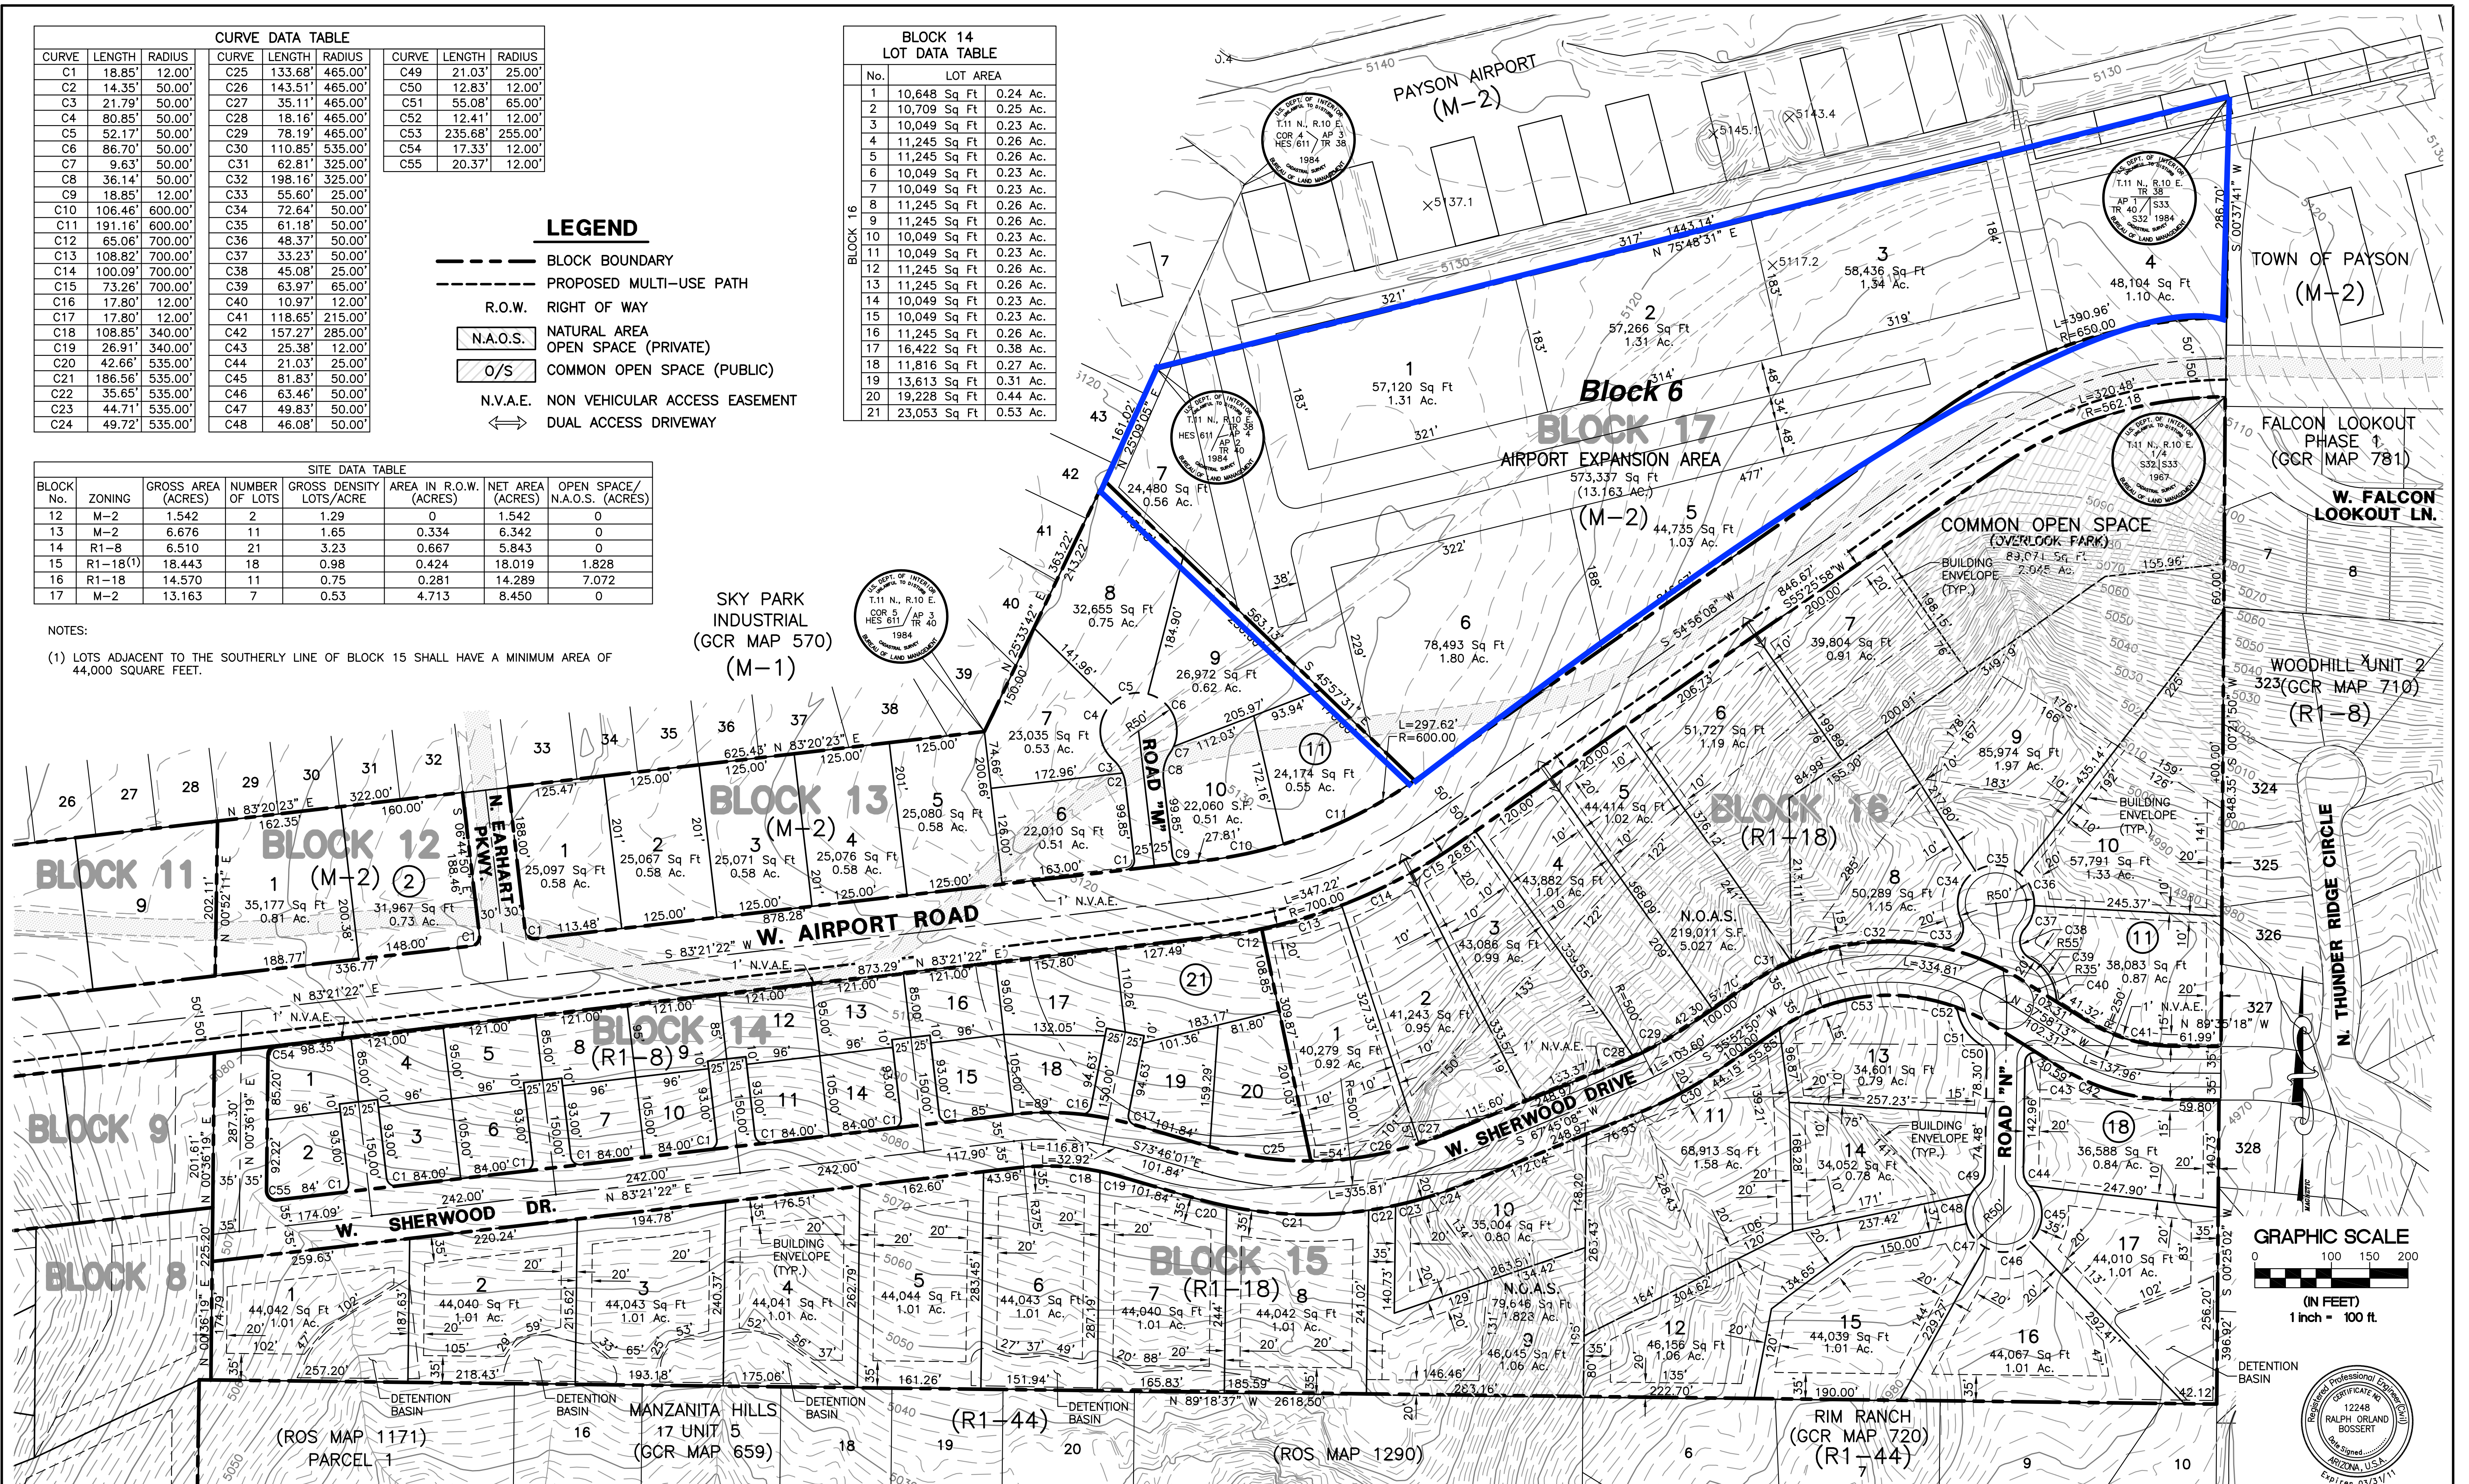

NO.	REVISIONS	DATE	BY	CHK.

Verde Engineering Group PLLC

1109 North McLane Road
Payson, Arizona 85541

Ralph Bossert P.E. R.L.S.
(928) 978-4345

Dan Fitzpatrick P.E.
(928) 595-2816

MONTEZUMA CASTLE LAND EXCHANGE

PAYSON, ARIZONA

JOB NO.	9016
DESIGNED BY:	RRH
DRAWN BY:	RRH
CHECKED BY:	ROB
APPROVED BY:	ROB
DATE:	05/12/10

REZONING SITE PLAN

BLOCKS 12-13-14-15-16 & 17

SCALE: HORIZ: 1" = 100'	
CONT. INTERVAL = 2'	
DRAWING NO.	SP4
SHEET NO. OF:	7 10